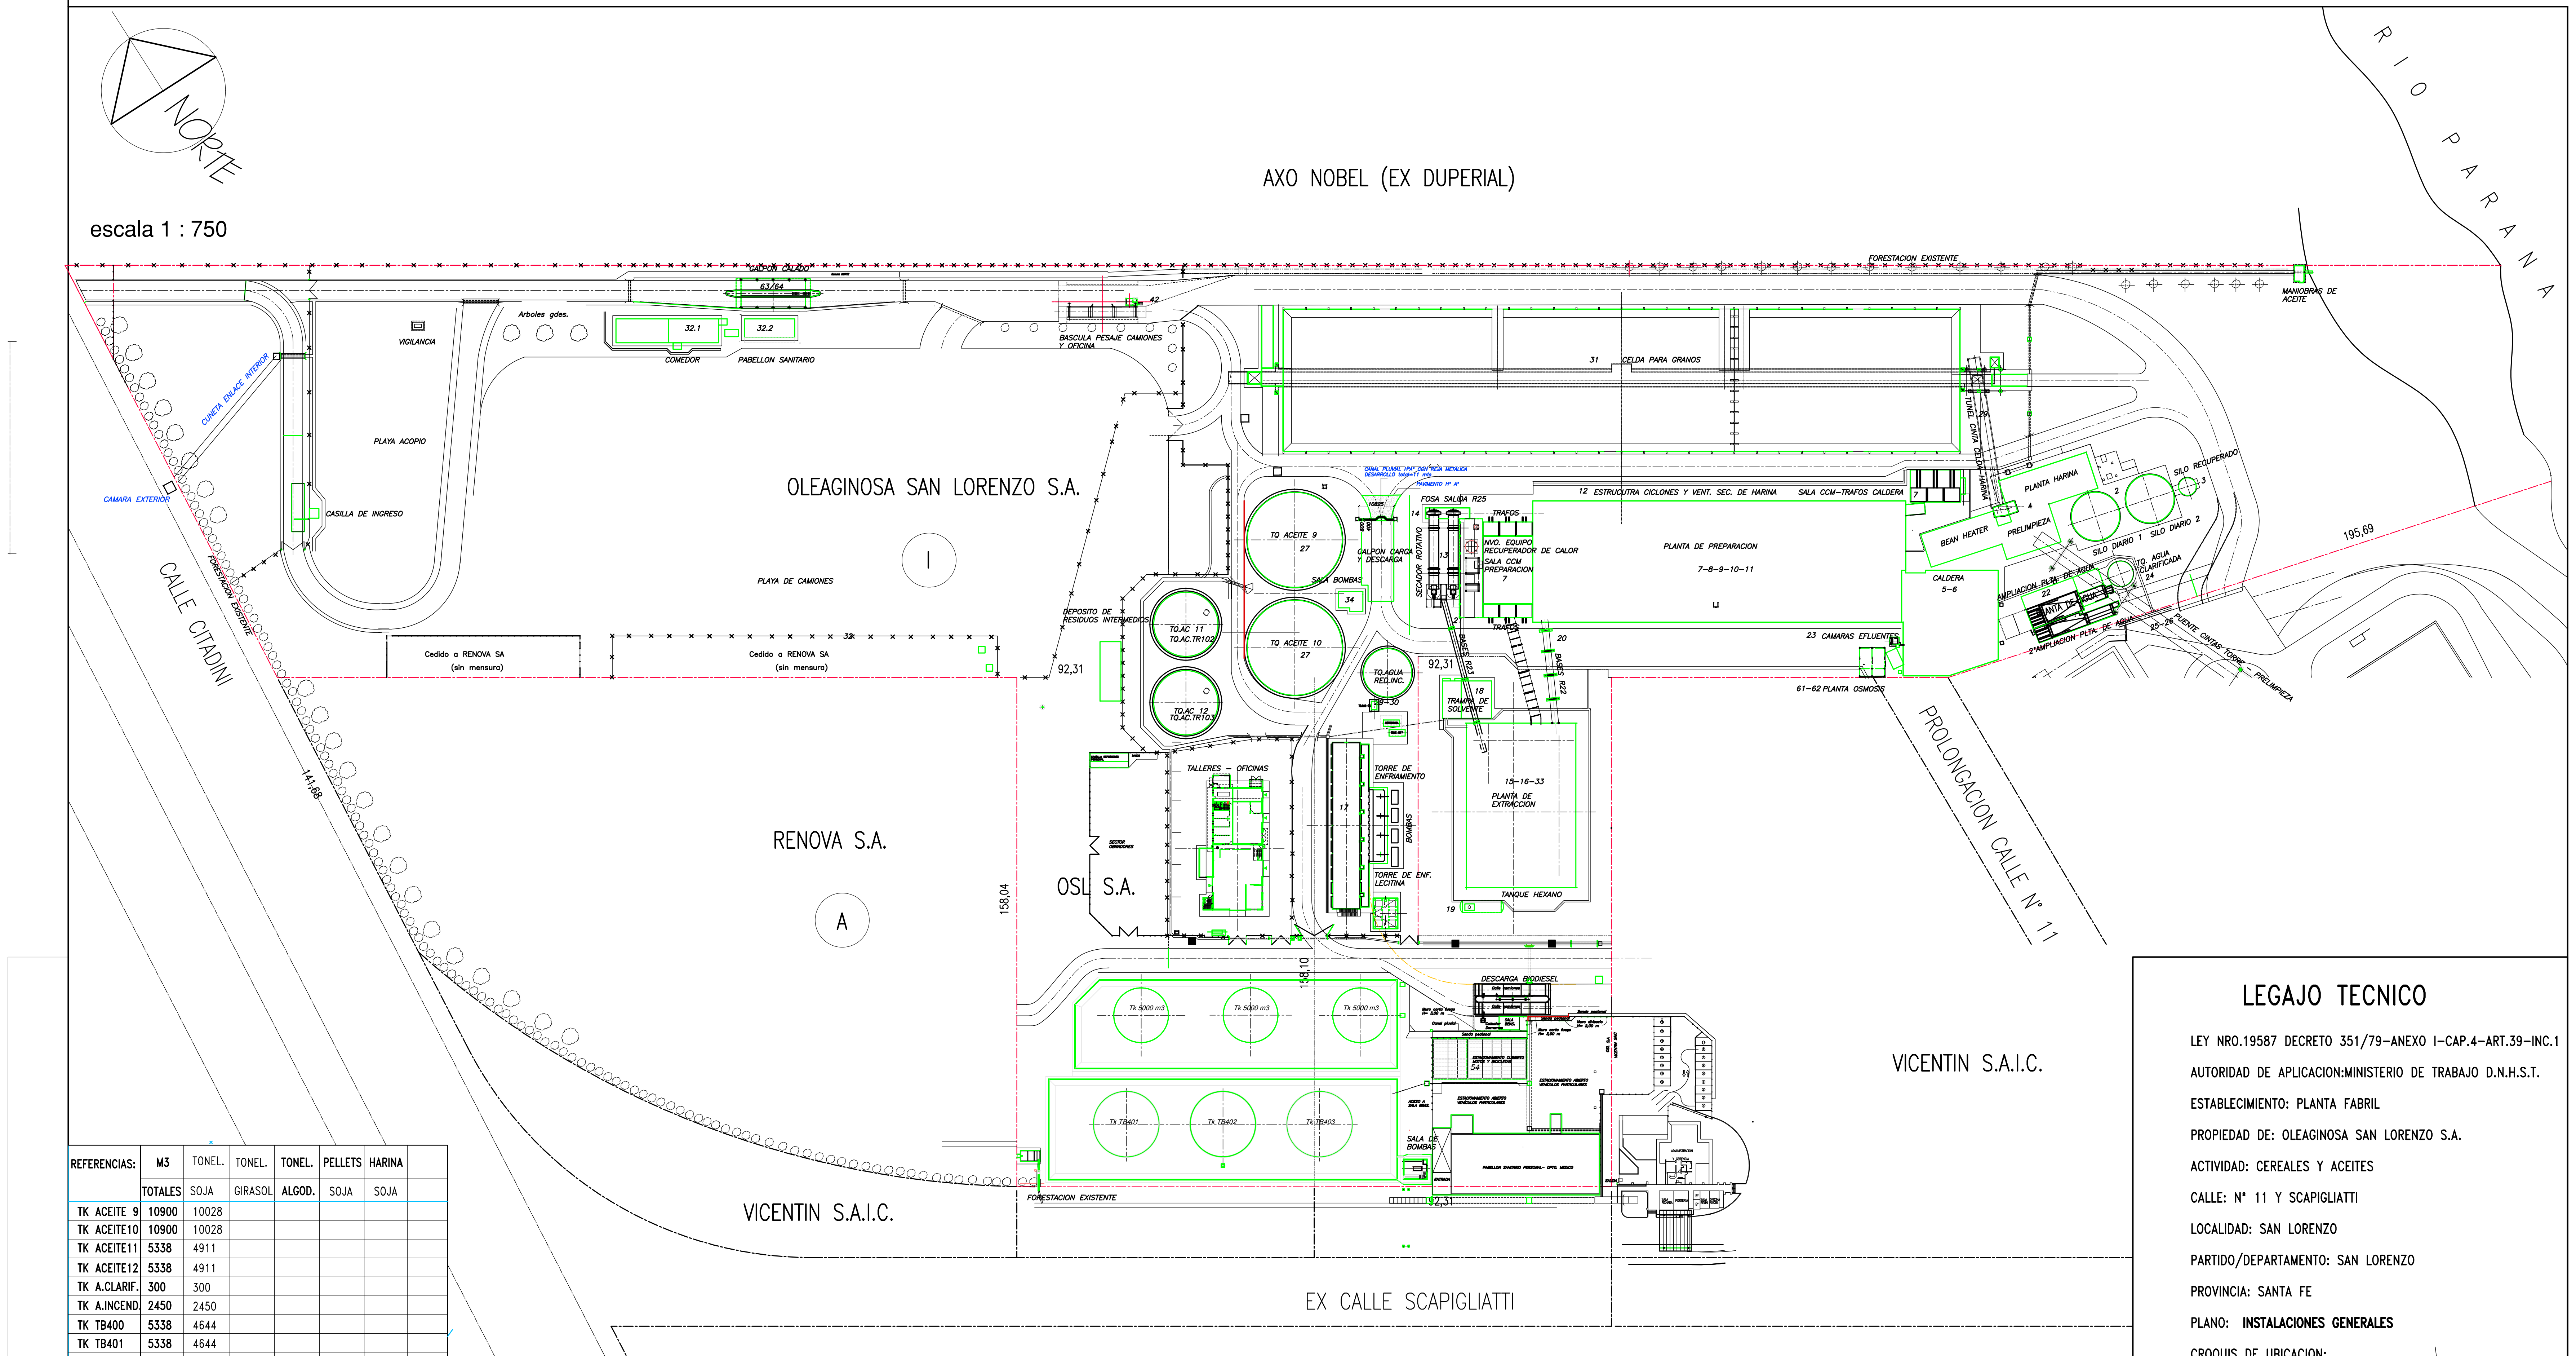
NORTE
escala 1 : 750
AXO NOBEL (EX DUPERIAL)
RIO PARANA
OLEAGINOSA SAN LORENZO S.A.
I
RENOVA S.A.
A
OSL S.A.
VICENTIN S.A.I.C.
VICENTIN S.A.I.C.
MOLINOS RIO DE LA PLATA
EX CALLE SCAPIGLIATTI
CALLE CITADINI
PROLONGACION CALLE Nº 11
FORESTACION EXISTENTE
GALPON CALADO
63/64
VIGILANCIA
Arboles gdes.
32.1
32.2
COMEDOR
PABELLON SANITARIO
BASCULA PESAJE CAMIONES Y OFICINA
42
CUNETA ENLACE INTERIOR
CAMARA EXTERIOR
PLAYA ACOPIO
CASILLA DE INGRESO
PLAYA DE CAMIONES
Cedido a RENOVA SA (sin mensura)
Cedido a RENOVA SA (sin mensura)
32
DEPOSITO DE RESIDUOS INTERMEDIOS
92,31
141,68
158,04
158,10
195,69
31 CELDA PARA GRANOS
CANAL PLUVIAL HºAº CON REJA METALICA DESARROLLO total=11 mts
PAVIMENTO Hº Aº
TQ ACEITE 9 27
TQ ACEITE 10 27
TQ.AC 11 TQ.AC.TR102
TQ.AC 12 TQ.AC.TR103
TQ.AGUA RED.INC.
29-30
GALPON CARGA Y DESCARGA
SALA BOMBAS
34
FOSA SALIDA R25
14
SECADOR ROTATIVO
13
TRAFOS
NVO. EQUIPO RECUPERADOR DE CALOR
SALA CCM PREPARACION 7
12 ESTRUCUTRA CICLONES Y VENT. SEC. DE HARINA
SALA CCM-TRAFOS CALDERA
7
PLANTA DE PREPARACION 7-8-9-10-11
21
BASES R23
20
BASES R22
23 CAMARAS EFLUENTES
61-62 PLANTA OSMOSIS
18 TRAMPA DE SOLVENTE
15-16-33 PLANTA DE EXTRACCION
TANQUE HEXANO
19
TALLERES - OFICINAS
SECTOR OBRADORES
17
TORRE DE ENFRIAMIENTO
BOMBAS
TORRE DE ENF. LECITINA
TUNEL CINTA CELDA-HARINA
29
PLANTA HARINA
4
BEAN HEATER
PRELIMPIEZA
CALDERA 5-6
SILO DIARIO 1
SILO DIARIO 2
2
SILO RECUPERADO
3
TQ. AGUA CLARIFICADA 24
AMPLIACION PLTA. DE AGUA
22
PLANTA DE AGUA
2ºAMPLIACION PLTA. DE AGUA
25-26
PUENTE CINTAS TORRE - PRELIMPIEZA
MANIOBRAS DE ACEITE
DESCARGA BIODIESEL
Calle camiones
Muro corta fuego H= 3,00 m
Canal pluvial
Colector Derrames
SALA BBAS.
Senda peatonal
Muro corta fuego H= 3,00 m
Muro divisorio H= 2,00 m
OSL SA
VICENTIN SAIC
ESTACIONAMIENTO CUBIERTO MOTOS Y BICICLETAS
54
ESTACIONAMIENTO ABIERTO VEHICULOS PARTICULARES
ACESO A SALA BBAS.
Tk 5000 m3
Tk 5000 m3
Tk 5000 m3
Tk TB401
Tk TB402
Tk TB403
SALA DE BOMBAS
ENTRADA
PABELLON SANITARIO PERSONAL- DPTO. MEDICO
SALIDA
ADMINISTRACION Y GERENCIA
SALA FICHADA
PORTERIA
SALA REUN
OFICINA RECIB.

REFERENCIAS:	M3	TONEL.	TONEL.	TONEL.	PELLETS	HARINA	
	TOTALES	SOJA	GIRASOL	ALGOD.	SOJA	SOJA	
TK ACEITE 9	10900	10028					
TK ACEITE10	10900	10028					
TK ACEITE11	5338	4911					
TK ACEITE12	5338	4911					
TK A.CLARIF.	300	300					
TK A.INCEND.	2450	2450					
TK TB400	5338	4644					
TK TB401	5338	4644					
TK TB402	5338	4644					
TK FO 403	5000	4900					
TK FO 404	5000	4900					
TK FO 405	5000	4900					
SILO DIARIO1	3125	2500					
SILO DIARIO2	3125	2500					
SILO REC.OSL	350	280					
CELDA 4	188800	151040			128384	120832	

PESOS ESPECIFICOS ADOPTADOS	
SEMILLA DE SOJA	0.8
PELLETS DE SOJA	0.68
HARINA DE SOJA	0.64
FUEL OIL	0.98
BIODIESEL	0.87
ACEITES	0.92

LEGAJO TECNICO

LEY NRO.19587 DECRETO 351/79-ANEXO I-CAP.4-ART.39-INC.1
AUTORIDAD DE APLICACION:MINISTERIO DE TRABAJO D.N.H.S.T.
ESTABLECIMIENTO: PLANTA FABRIL
PROPIEDAD DE: OLEAGINOSA SAN LORENZO S.A.
ACTIVIDAD: CEREALES Y ACEITES
CALLE: Nº 11 Y SCAPIGLIATTI
LOCALIDAD: SAN LORENZO
PARTIDO/DEPARTAMENTO: SAN LORENZO
PROVINCIA: SANTA FE
PLANO: **INSTALACIONES GENERALES**
CROQUIS DE UBICACION:

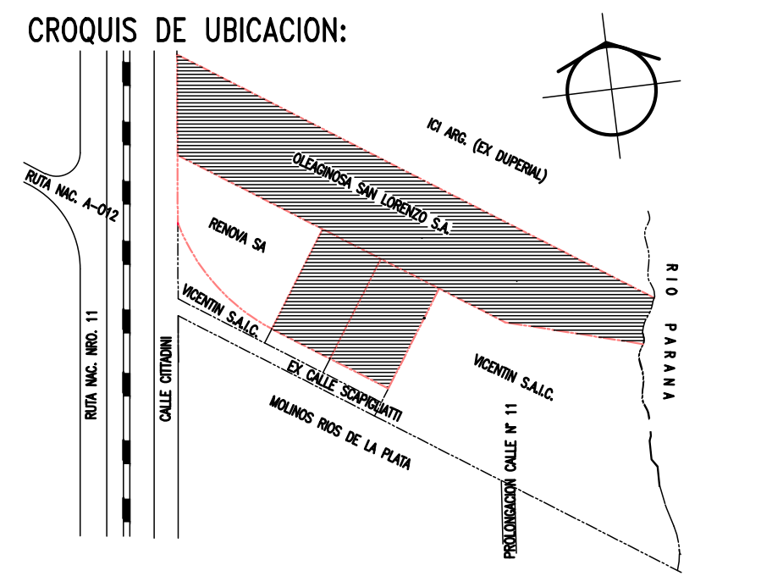
ICI ARG. (EX DUPERIAL)
OLEAGINOSA SAN LORENZO S.A.
RENOVA SA
VICENTIN S.A.I.C.
VICENTIN S.A.I.C.
EX CALLE SCAPIGLIATTI
MOLINOS RIOS DE LA PLATA
RUTA NAC. A-012
RUTA NAC. NRO. 11
CALLE CITTADINI
PROLONGACION CALLE Nº 11
RIO PARANA

FIRMA PROPIETARIO REPRESENTANTE

JEFE SERVICIO SeHT:
REG.NAC.GRAD.UNIV.NRO. LEY 19587
DEC.351/79-PEN-CAP.4-ART.35Y37-INC.3
REVISION: 22 ABRIL 2023 PLNº3371A