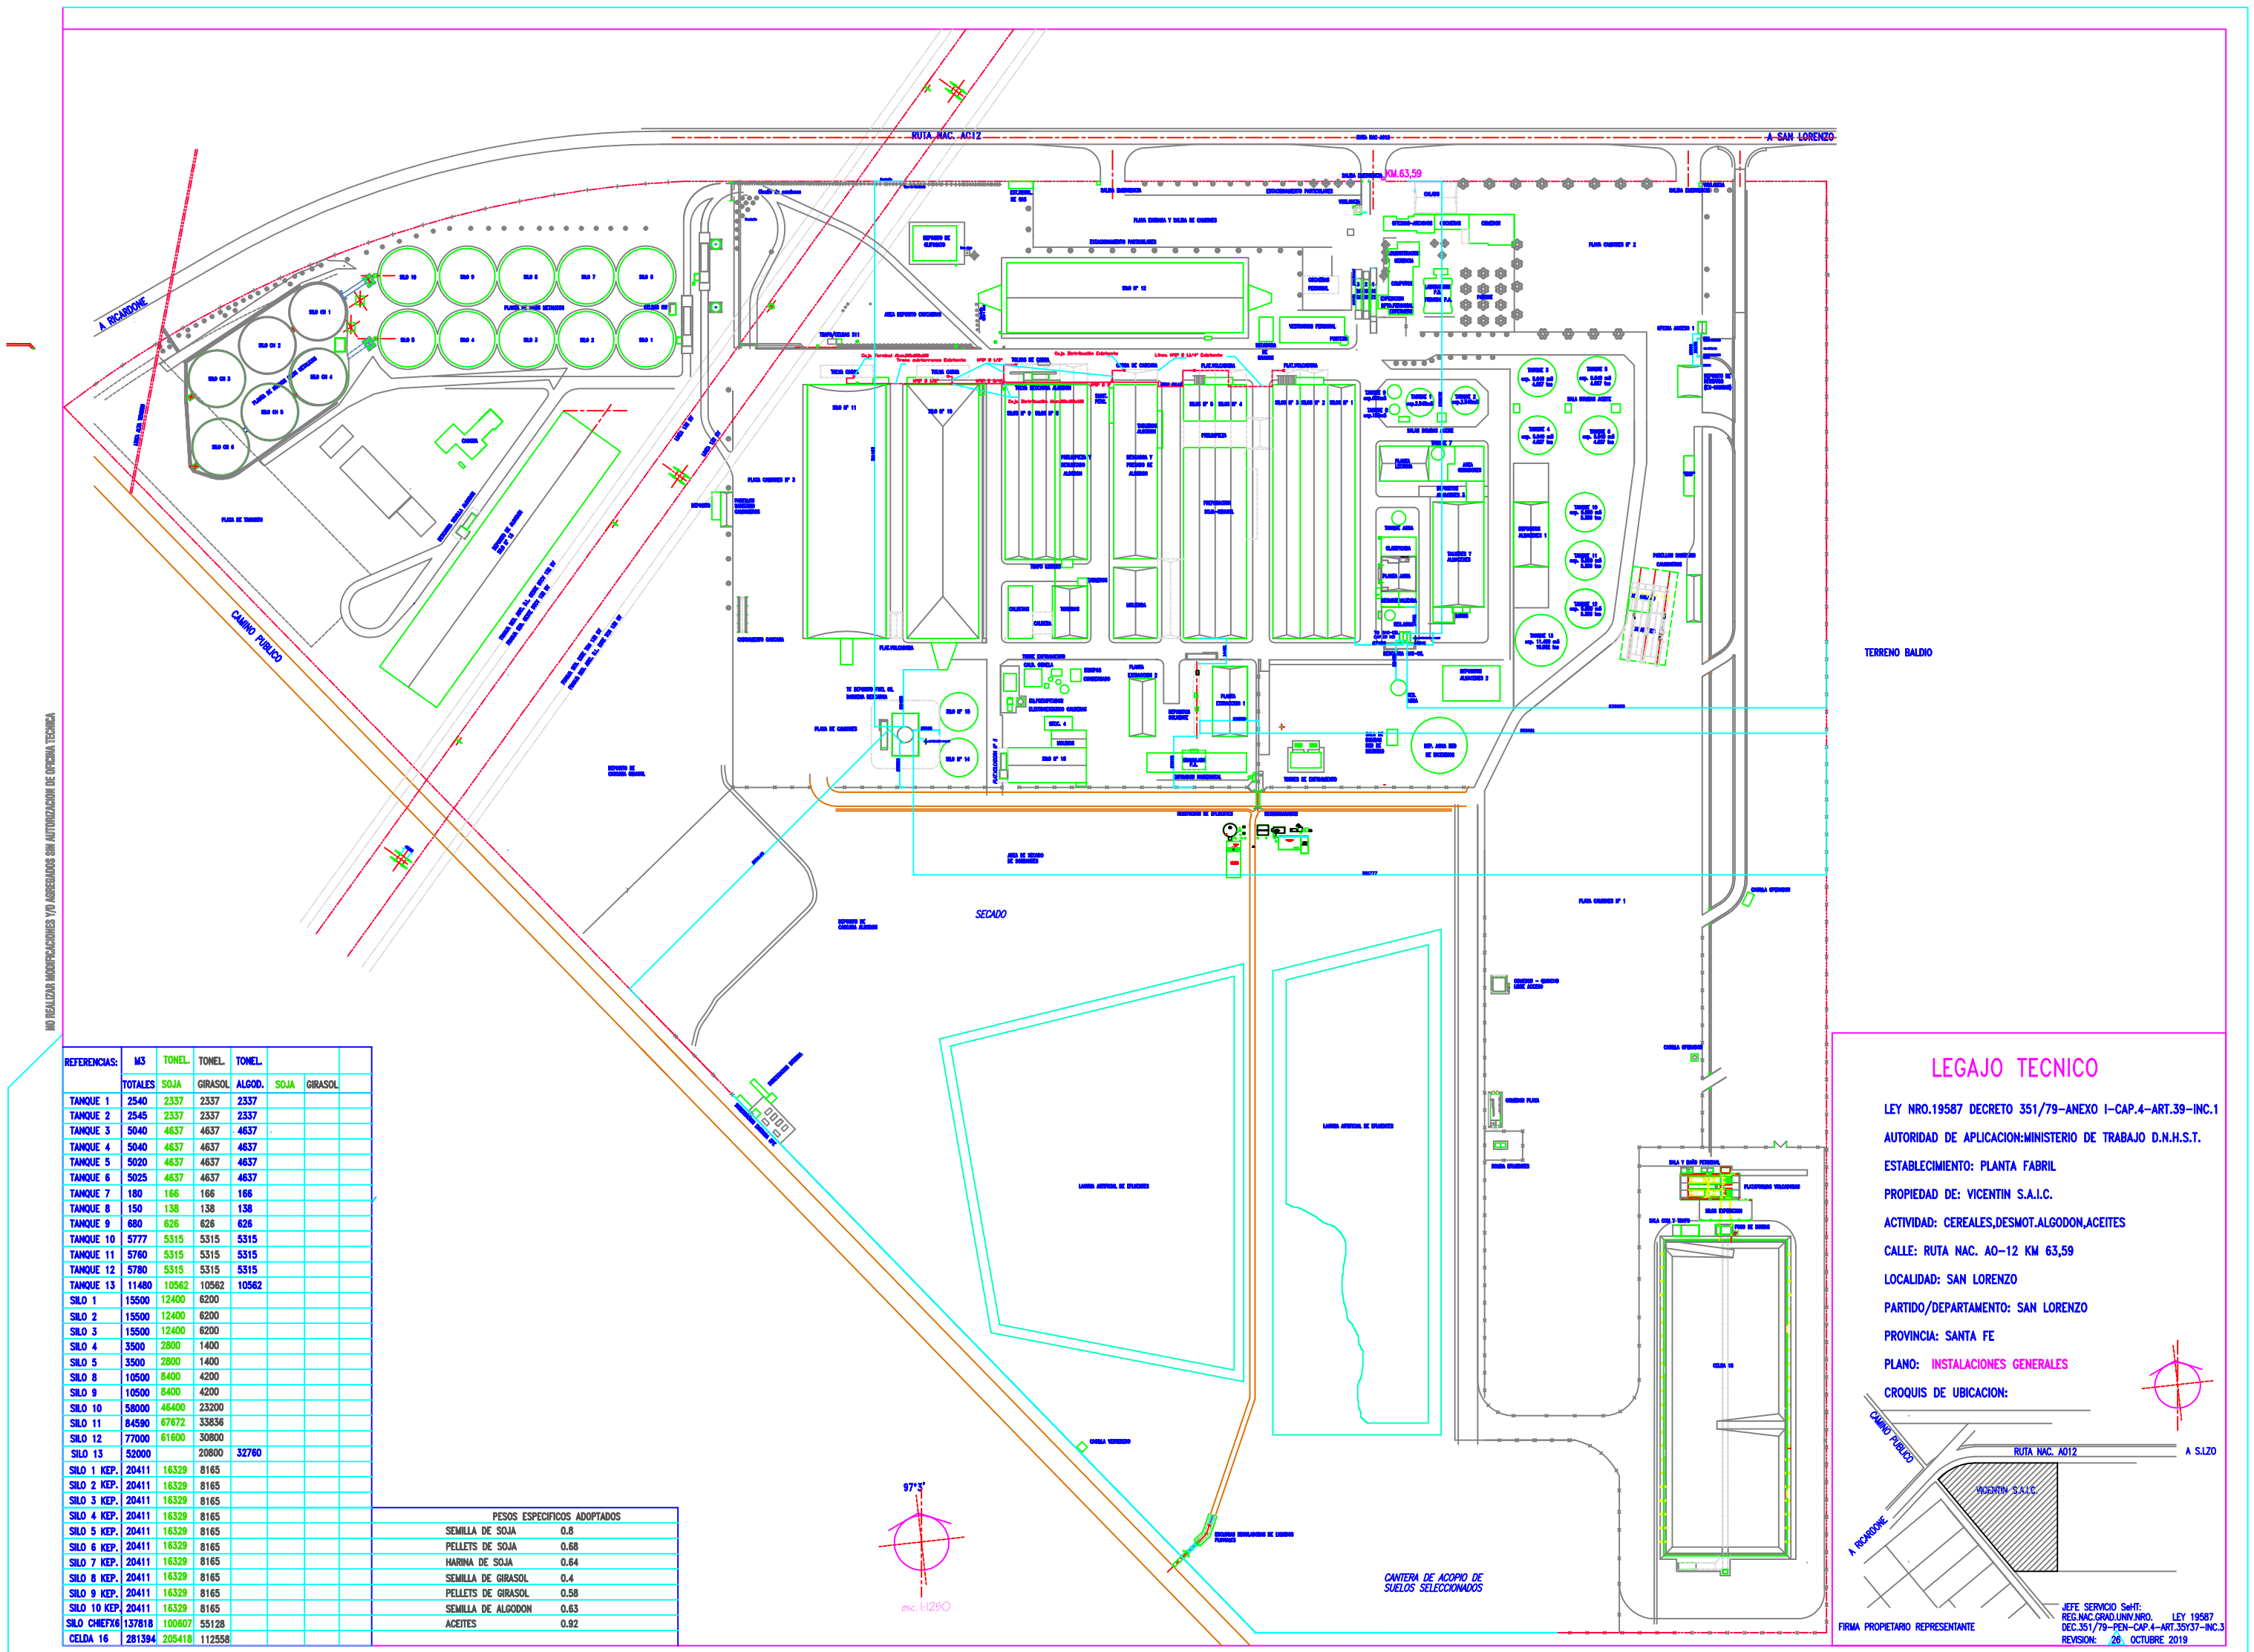


REFERENCIAS:	M3	TONEL.	TONEL.	TONEL.			
	TOTALES	SOJA	GIRASOL	ALGOD.	SOJA	GIRASOL	
TANQUE 1	2540	2337	2337	2337			
TANQUE 2	2545	2337	2337	2337			
TANQUE 3	5040	4637	4637	4637			
TANQUE 4	5040	4637	4637	4637			
TANQUE 5	5020	4637	4637	4637			
TANQUE 6	5025	4637	4637	4637			
TANQUE 7	180	166	166	166			
TANQUE 8	150	138	138	138			
TANQUE 9	680	626	626	626			
TANQUE 10	5777	5315	5315	5315			
TANQUE 11	5760	5315	5315	5315			
TANQUE 12	5780	5315	5315	5315			
TANQUE 13	11480	10562	10562	10562			
SILO 1	15500	12400	6200				
SILO 2	15500	12400	6200				
SILO 3	15500	12400	6200				
SILO 4	3500	2800	1400				
SILO 5	3500	2800	1400				
SILO 8	10500	8400	4200				
SILO 9	10500	8400	4200				
SILO 10	58000	46400	23200				
SILO 11	84590	67672	33836				
SILO 12	77000	61600	30800				
SILO 13	52000		20800	32760			
SILO 1 KEP.	20411	16329	8165				
SILO 2 KEP.	20411	16329	8165				
SILO 3 KEP.	20411	16329	8165				
SILO 4 KEP.	20411	16329	8165				
SILO 5 KEP.	20411	16329	8165				
SILO 6 KEP.	20411	16329	8165				
SILO 7 KEP.	20411	16329	8165				
SILO 8 KEP.	20411	16329	8165				
SILO 9 KEP.	20411	16329	8165				
SILO 10 KEP.	20411	16329	8165				
SILO CHIEFX6	137818	100607	55128				
CELDA 16	281394	205418	112558				

PESOS ESPECIFICOS ADOPTADOS	
SEMILLA DE SOJA	0.8
PELLETS DE SOJA	0.68
HARINA DE SOJA	0.64
SEMILLA DE GIRASOL	0.4
PELLETS DE GIRASOL	0.58
SEMILLA DE ALGODON	0.63
ACEITES	0.92

LEGAJO TECNICO

LEY NRO.19587 DECRETO 351/79-ANEXO I-CAP.4-ART.39-INC.1

AUTORIDAD DE APLICACION:MINISTERIO DE TRABAJO D.N.H.S.T.

ESTABLECIMIENTO: PLANTA FABRIL

PROPIEDAD DE: VICENTIN S.A.I.C.

ACTIVIDAD: CEREALES,DESMOT.ALGODON,ACEITES

CALLE: RUTA NAC. AO-12 KM 63,59

LOCALIDAD: SAN LORENZO

PARTIDO/DEPARTAMENTO: SAN LORENZO

PROVINCIA: SANTA FE

PLANO: INSTALACIONES GENERALES

CROQUIS DE UBICACION:

FIRMA PROPIETARIO REPRESENTANTE

JEFE SERVICIO SeHT:
REG.NAC.GRAD.UNIV.NRO. LEY 19587
DEC.351/79-PEN-CAP.4-ART.35Y37-INC.3
REVISION: 26 OCTUBRE 2019